
HOOP HUB · FLOOR MARKINGS PLAN

Example for floor tile suppliers · covered hub floor · scale 1:75 at A3 · dimensions in metres

Main hoop end at the top. 3x3 markings to FIBA measurements from the inner edge of the white baseline.

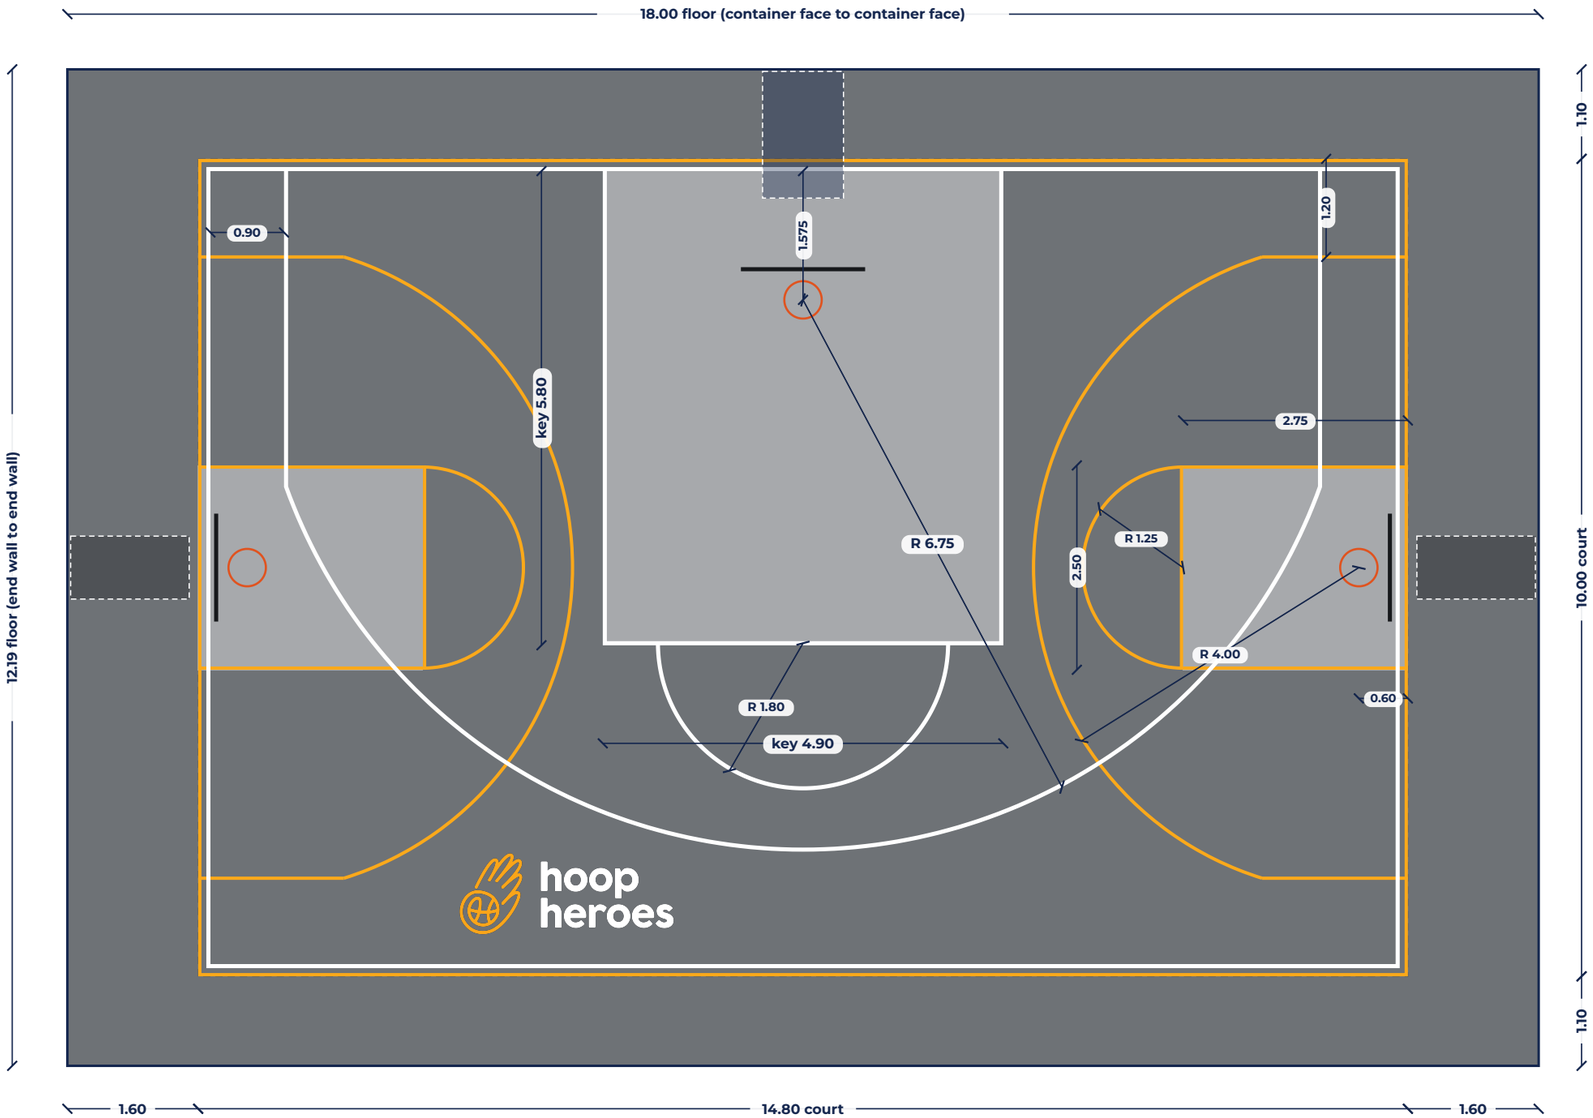

COLOURS

- **Court and run-off tiles**
  mid grey · #6e7276
- **Keys (3x3 and both mini)**
  light grey · #a7a9ac
- **3x3 lines**
  white · 50 mm wide
- **Mini court lines**
  Hoop Heroes gold · #fba91a · 40 mm wide

MARKINGS

3x3 (white): boundary 0.10 m inside the court edge; key 4.90 x 5.80 m; free-throw semicircle R 1.80 m; three-point line R 6.75 m from the basket centre (1.575 m from the baseline), straight 0.90 m in from the sidelines. No no-charge semicircle.
Mini court (gold): played across, between the 10 m sides. Boundary on the court edge; at each end a 2.75 x 2.50 m key, free-throw semicircle R 1.25 m and three-point line R 4.00 m from the rim (0.60 m in), straight 1.20 m in from the 14.8 m sides.
No halfway line or centre circle.
Logo: Hoop Heroes, about 3.0 x 1.4 m, open end, left of centre (artwork to be supplied).

FOR THE SUPPLIER

Whole floor 18.00 x 12.19 m (219 m²), indoors under a fabric canopy, laid on school playground tarmac. Run-off in the same grey as the court.
Please propose tile type, size and layout, and how the lines are applied (printed, inlaid or painted).
Main portable hoop base (155 x 99 cm, about 260 kg plus ballast) sits partly on the court; mini hoop bases sit on the run-off. Dashed outlines show them for reference; they are not markings.
Court is sized to the floor, not to the full FIBA 3x3 court (15 x 11 m).

Concept only · confirm all dimensions on site