
HERO DOME · FLOOR MARKINGS PLAN · MULTI–SPORT WITH 3x3

Example for floor tile suppliers · covered hub floor · scale 1:75 at A3 · dimensions in metres

For 5 to 11-year-olds: mini basketball across the court, dodgeball and three children's pickleball / badminton courts.

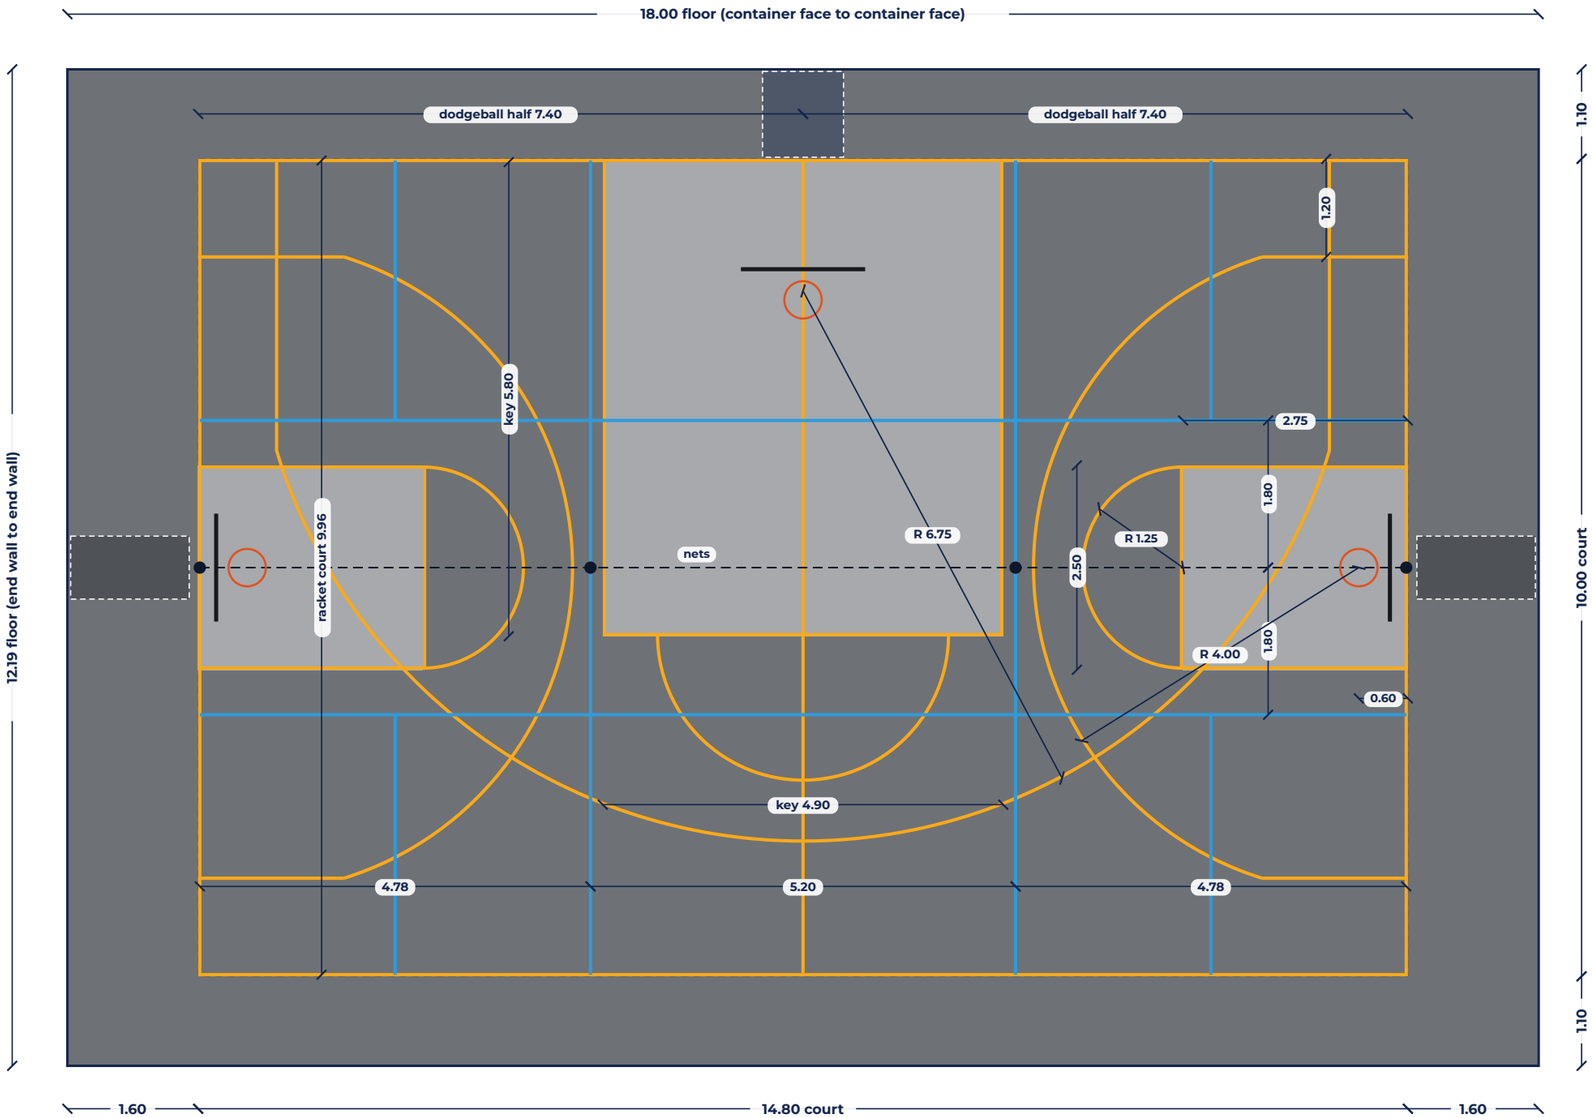

COLOURS

- **Court and run-off tiles**
  mid grey · #6e7276
- **Keys (3x3 and both mini)**
  light grey · #a7a9ac
- **Basketball (mini and 3x3) and dodgeball**
  Hoop Heroes gold · #fba91a · 40 mm wide
- **Pickleball / badminton**
  blue · #2f9bdc · 40 mm wide

MARKINGS

Mini basketball (gold), the main court: played across, between the 10 m sides. Keys 2.75 x 2.50 m, free-throw semicircles R 1.25 m, three-point lines R 4.00 m from the rim (0.60 m in), corners 1.20 m in. Dodgeball (gold): the mini court boundary plus a halfway line: two halves of 7.40 x 10.00 m. Pickleball / badminton (blue): three children's courts inside the gold boundary, 4.78 / 5.20 / 4.78 m wide and 9.96 m long (to line centres), portable nets across the middle. Service (non-volley) lines 1.80 m from the net; centre lines to the ends. The gold halfway line is the middle court's centre line. 3x3 (gold): key 4.90 x 5.80 m filled light grey, free-throw semicircle R 1.80 m, three-point line R 6.75 m with 0.90 m corners, all from the gold boundary as the baseline. No logo.

FOR THE SUPPLIER

Whole floor 18.00 x 12.19 m (219 m²), indoors under a fabric canopy, laid on school playground tarmac. Run-off in the same grey as the court. Not to official sizes: laid out for 5 to 11-year-olds to make the most of the floor. Please propose tile type, size and layout, and how the lines are applied (printed, inlaid or painted). Net posts: freestanding, at the dots on the net line. Hoop bases: dashed outlines, for reference only.

CONCEPT - HERO DOME

Concept only · confirm all dimensions on site