
HEROES ARENA · FLOOR MARKINGS PLAN

Example for floor tile suppliers · covered hub floor · scale 1:75 at A3 · dimensions in metres

Main hoop end at the top. 3x3 markings to FIBA measurements from the inner edge of the white baseline.

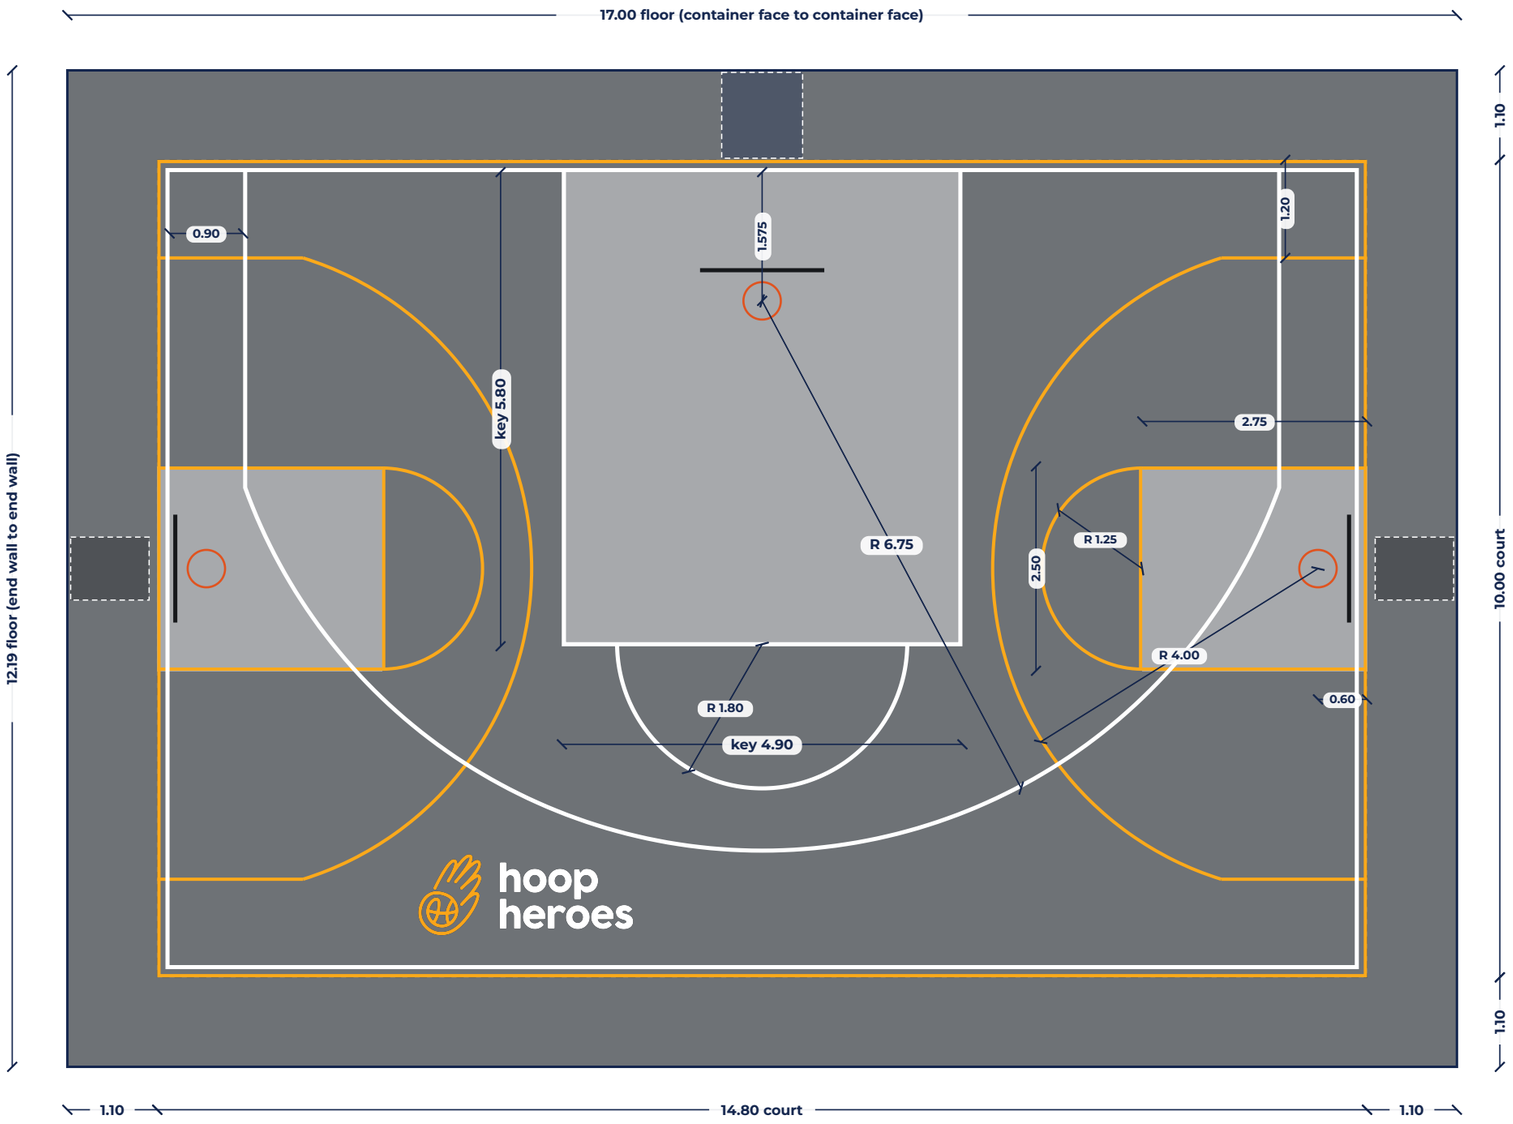

COLOURS

- **Court and run-off tiles**
  mid grey · #6e7276
- **Keys (3x3 and both mini)**
  light grey · #a7a9ac
- **3x3 lines**
  white · 50 mm wide
- **Mini court lines**
  Hoop Heroes gold · #fba91a · 40 mm wide

MARKINGS

3x3 (white): boundary 0.10 m inside the court edge; key 4.90 x 5.80 m; free-throw semicircle R 1.80 m; three-point line R 6.75 m from the basket centre (1.575 m from the baseline), straight 0.90 m in from the sidelines. No no-charge semicircle.
Mini court (gold): played across, between the 10 m sides. Boundary on the court edge; at each end a 2.75 x 2.50 m key, free-throw semicircle R 1.25 m and three-point line R 4.00 m from the rim (0.60 m in), straight 1.20 m in from the 14.8 m sides.
No halfway line or centre circle.
Logo: Hoop Heroes, about 3.0 x 1.4 m, open end, left of centre (artwork to be supplied).

FOR THE SUPPLIER

Whole floor 17.00 x 12.19 m (207 m²), indoors under a fabric canopy, laid on school playground tarmac.
Run-off in the same grey as the court.
Please propose tile type, size and layout, and how the lines are applied (printed, inlaid or painted).
Main portable hoop base sits behind the baseline (drawn about 105 x 99 cm; size to confirm); mini hoop bases sit on the run-off. Dashed outlines show them for reference; they are not markings.
Court is sized to the floor, not to the full FIBA 3x3 court (15 x 11 m).

CONCEPT - HEROES ARENA

Concept only · confirm all dimensions on site